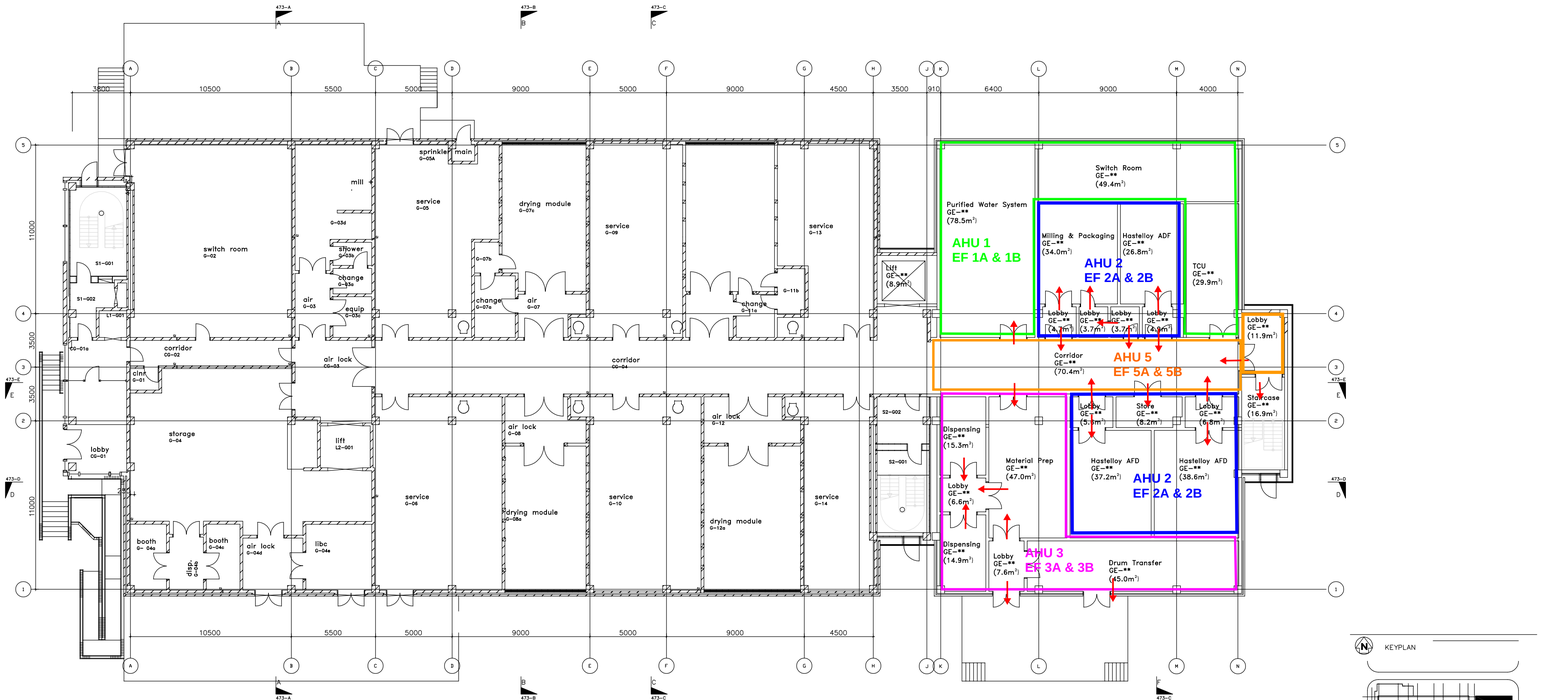


# PRESSURE REGIME & AHU ZONING LAYOUT
# GROUND FLOOR

Scitech EKIUM

DRAWING No.: 300291-BS-SK-0001

DATE: 22/05/26 SCALE: 1:200 REV: P1