


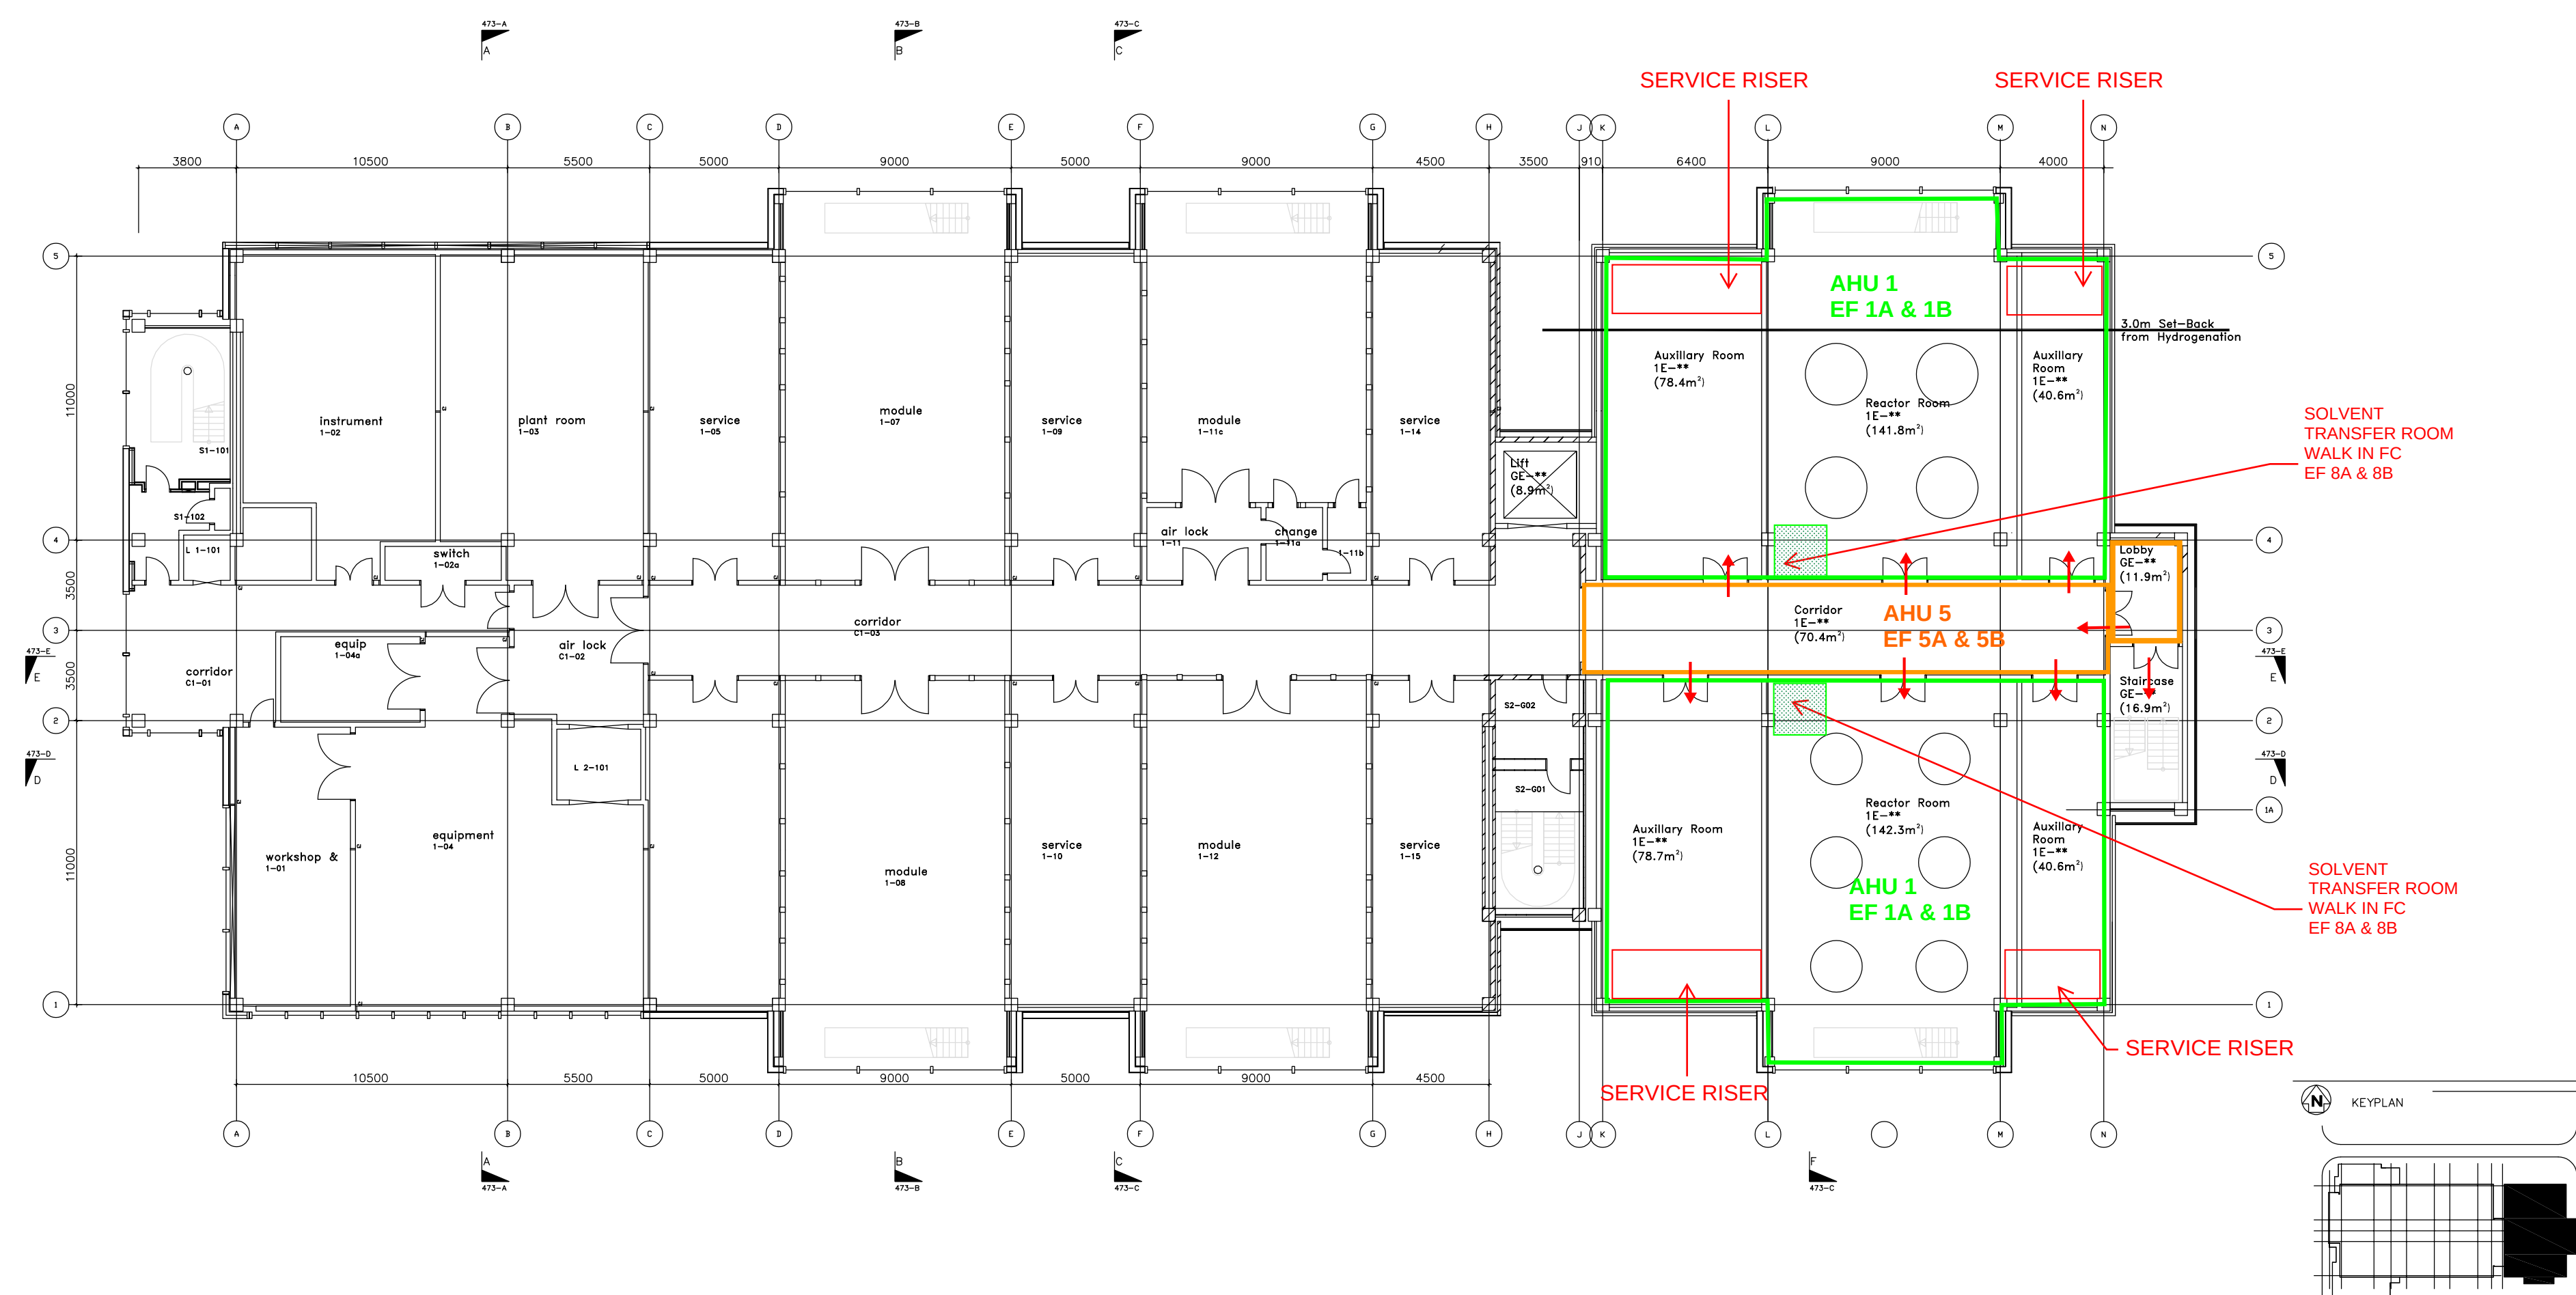

PRESSURE REGIME & AHU ZONING LAYOUT FIRST FLOOR