


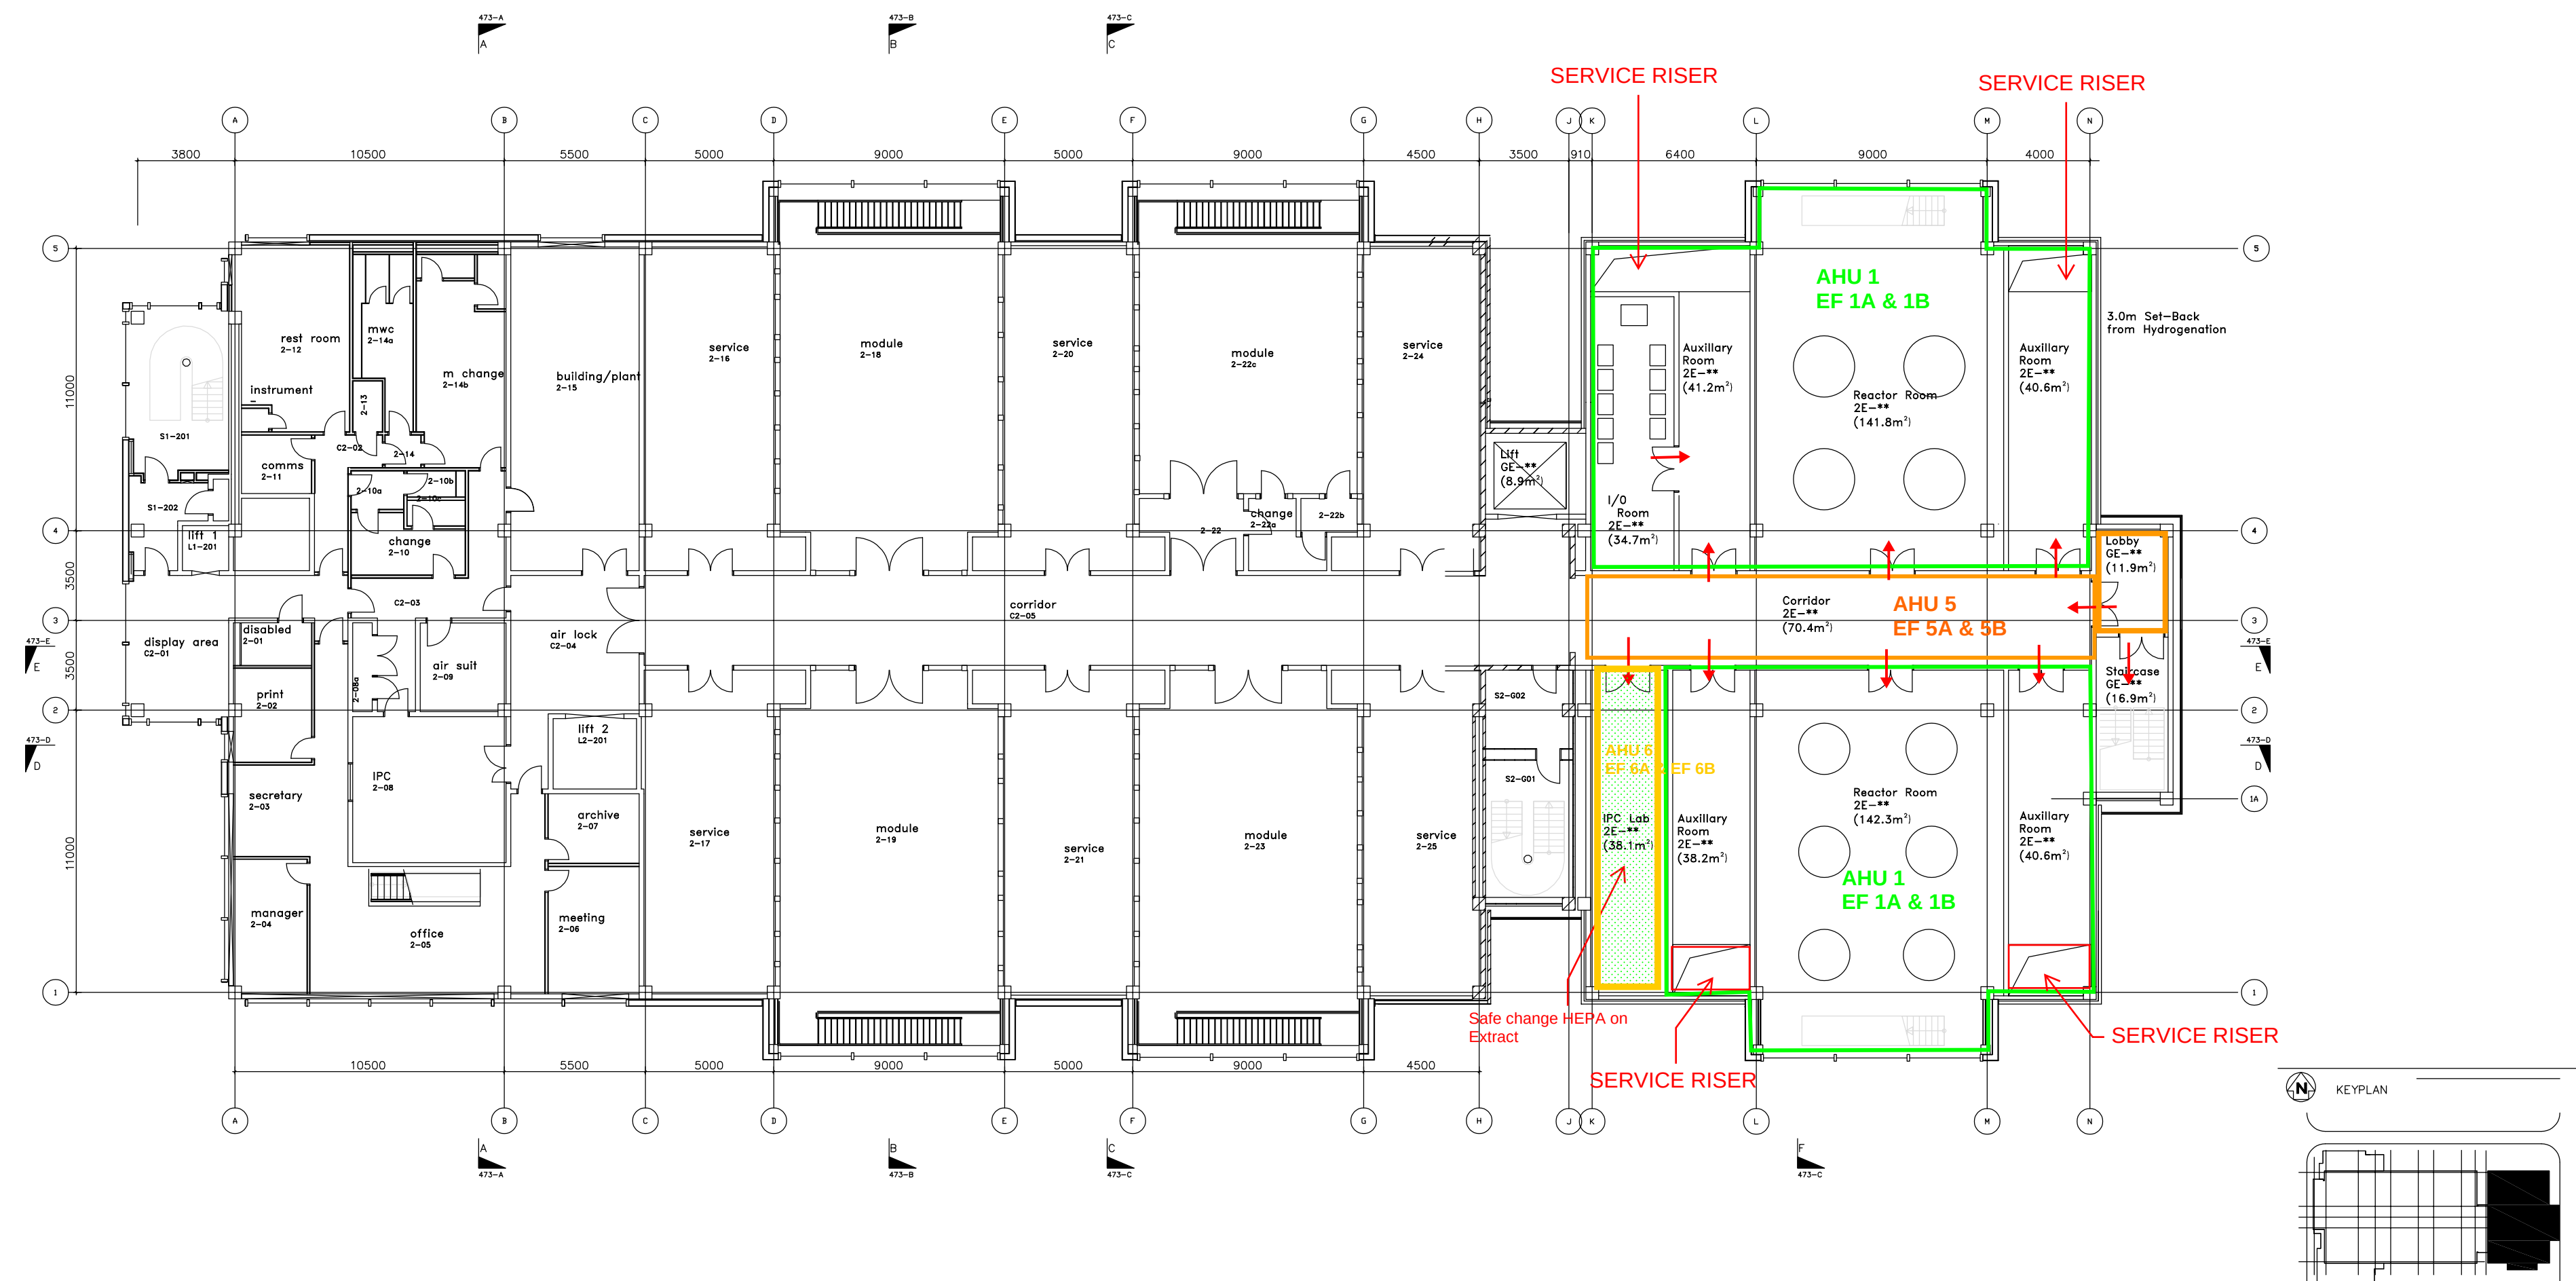

PRESSURE REGIME & AHU ZONING LAYOUT SECOND FLOOR