


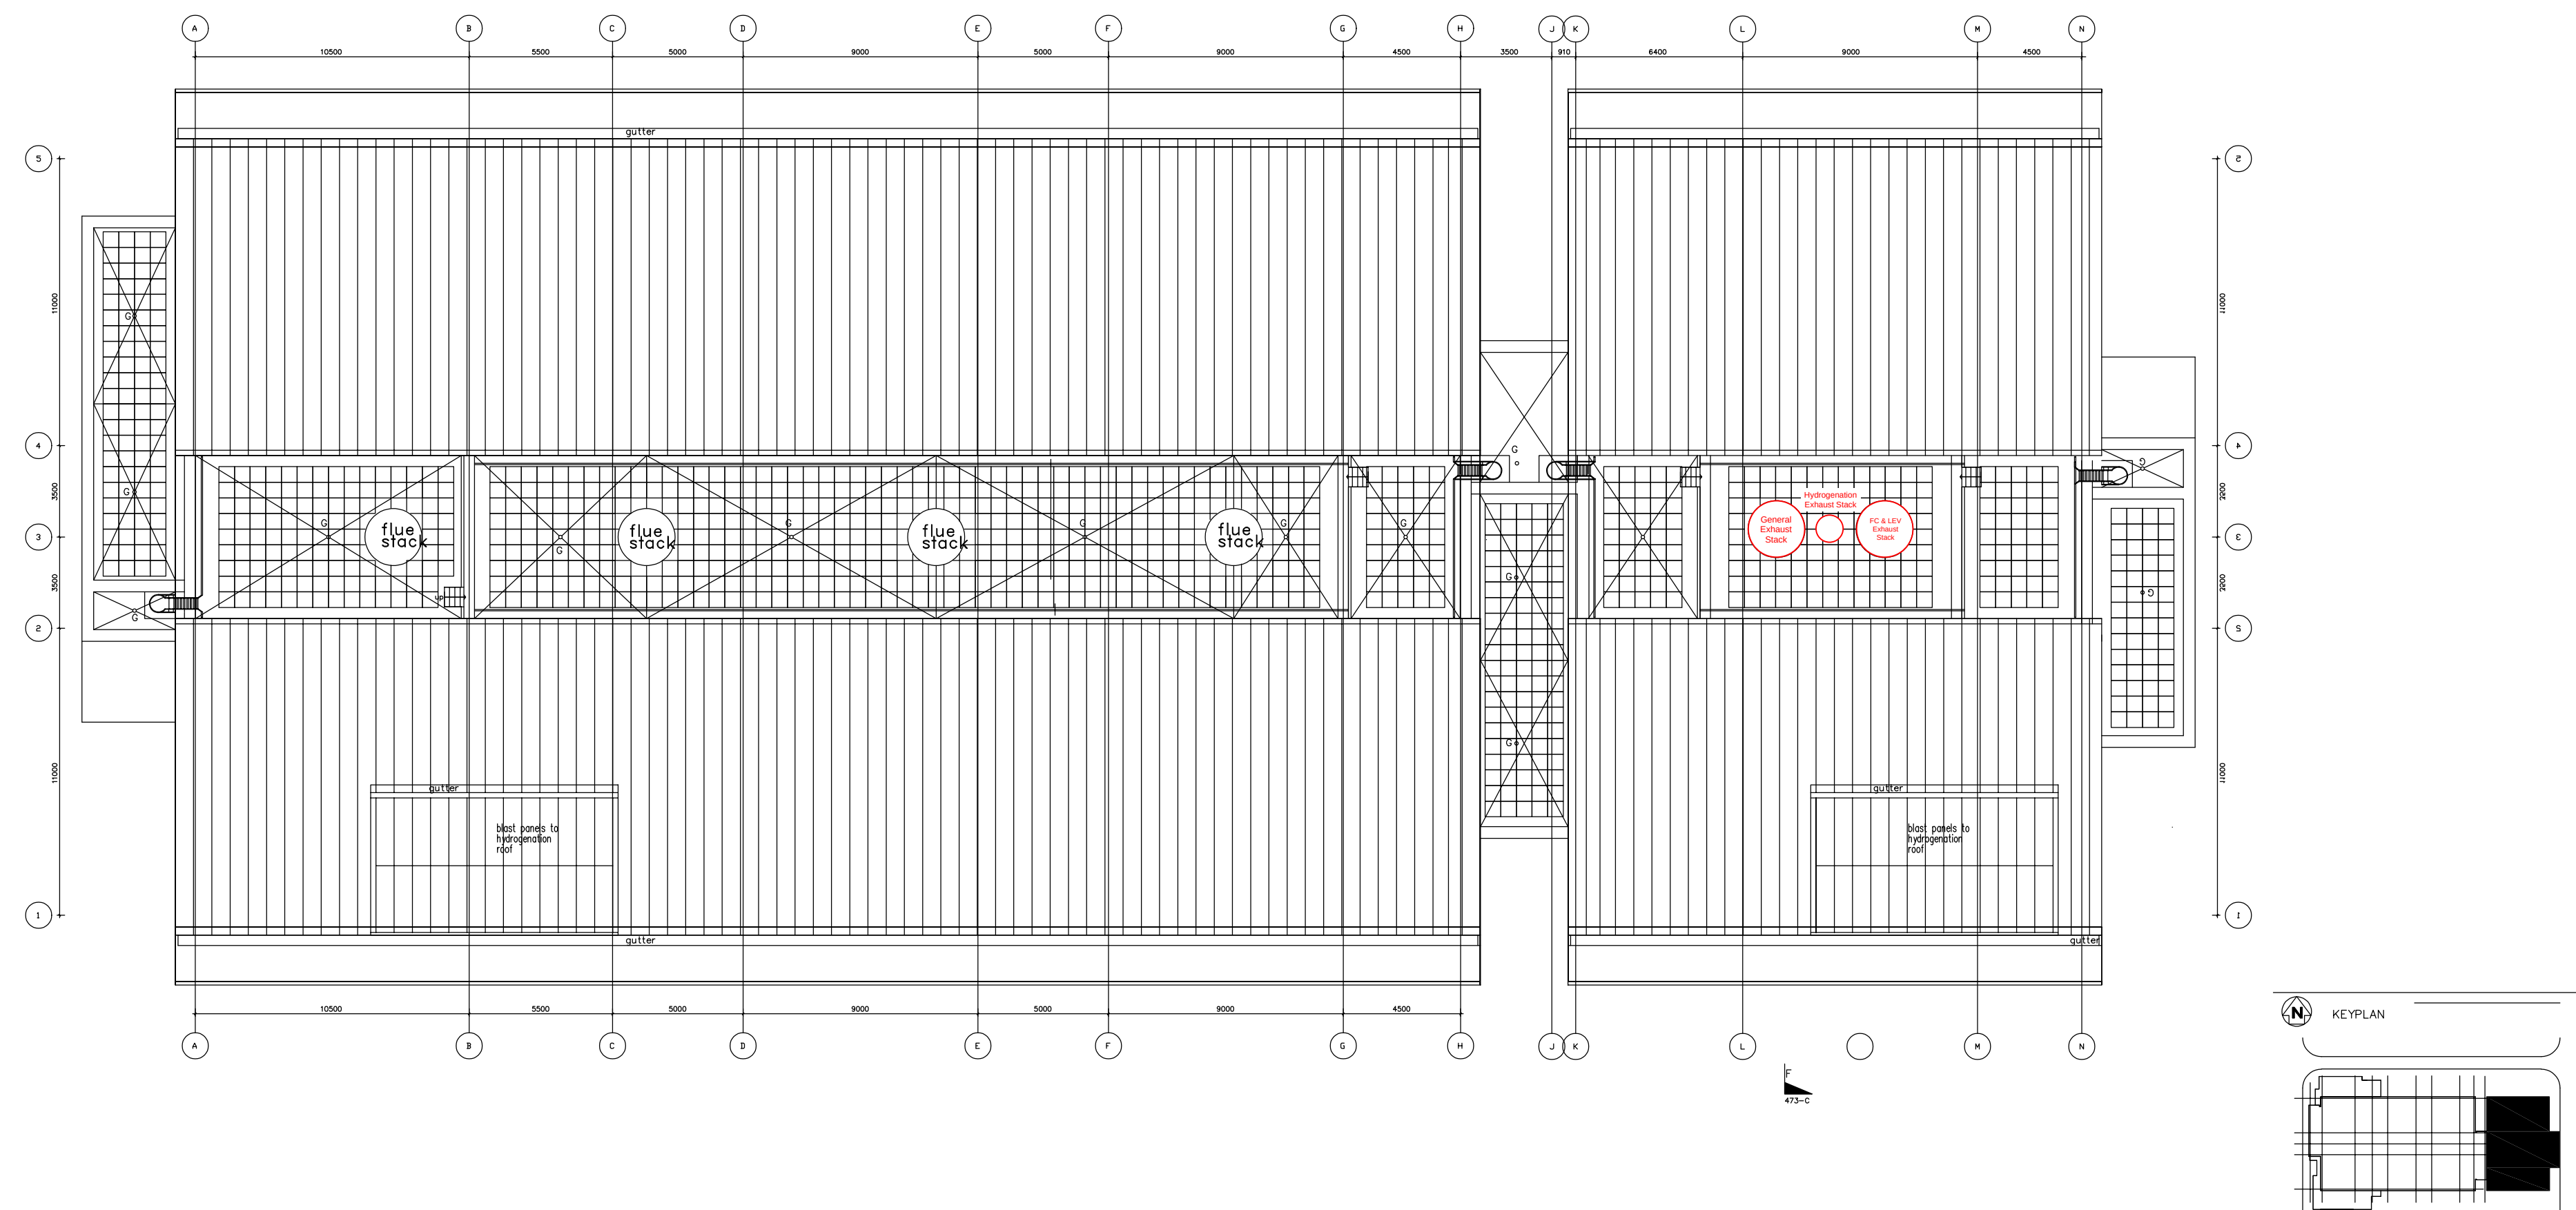

PRESSURE REGIME & AHU ZONING LAYOUT ROOF FLOOR