


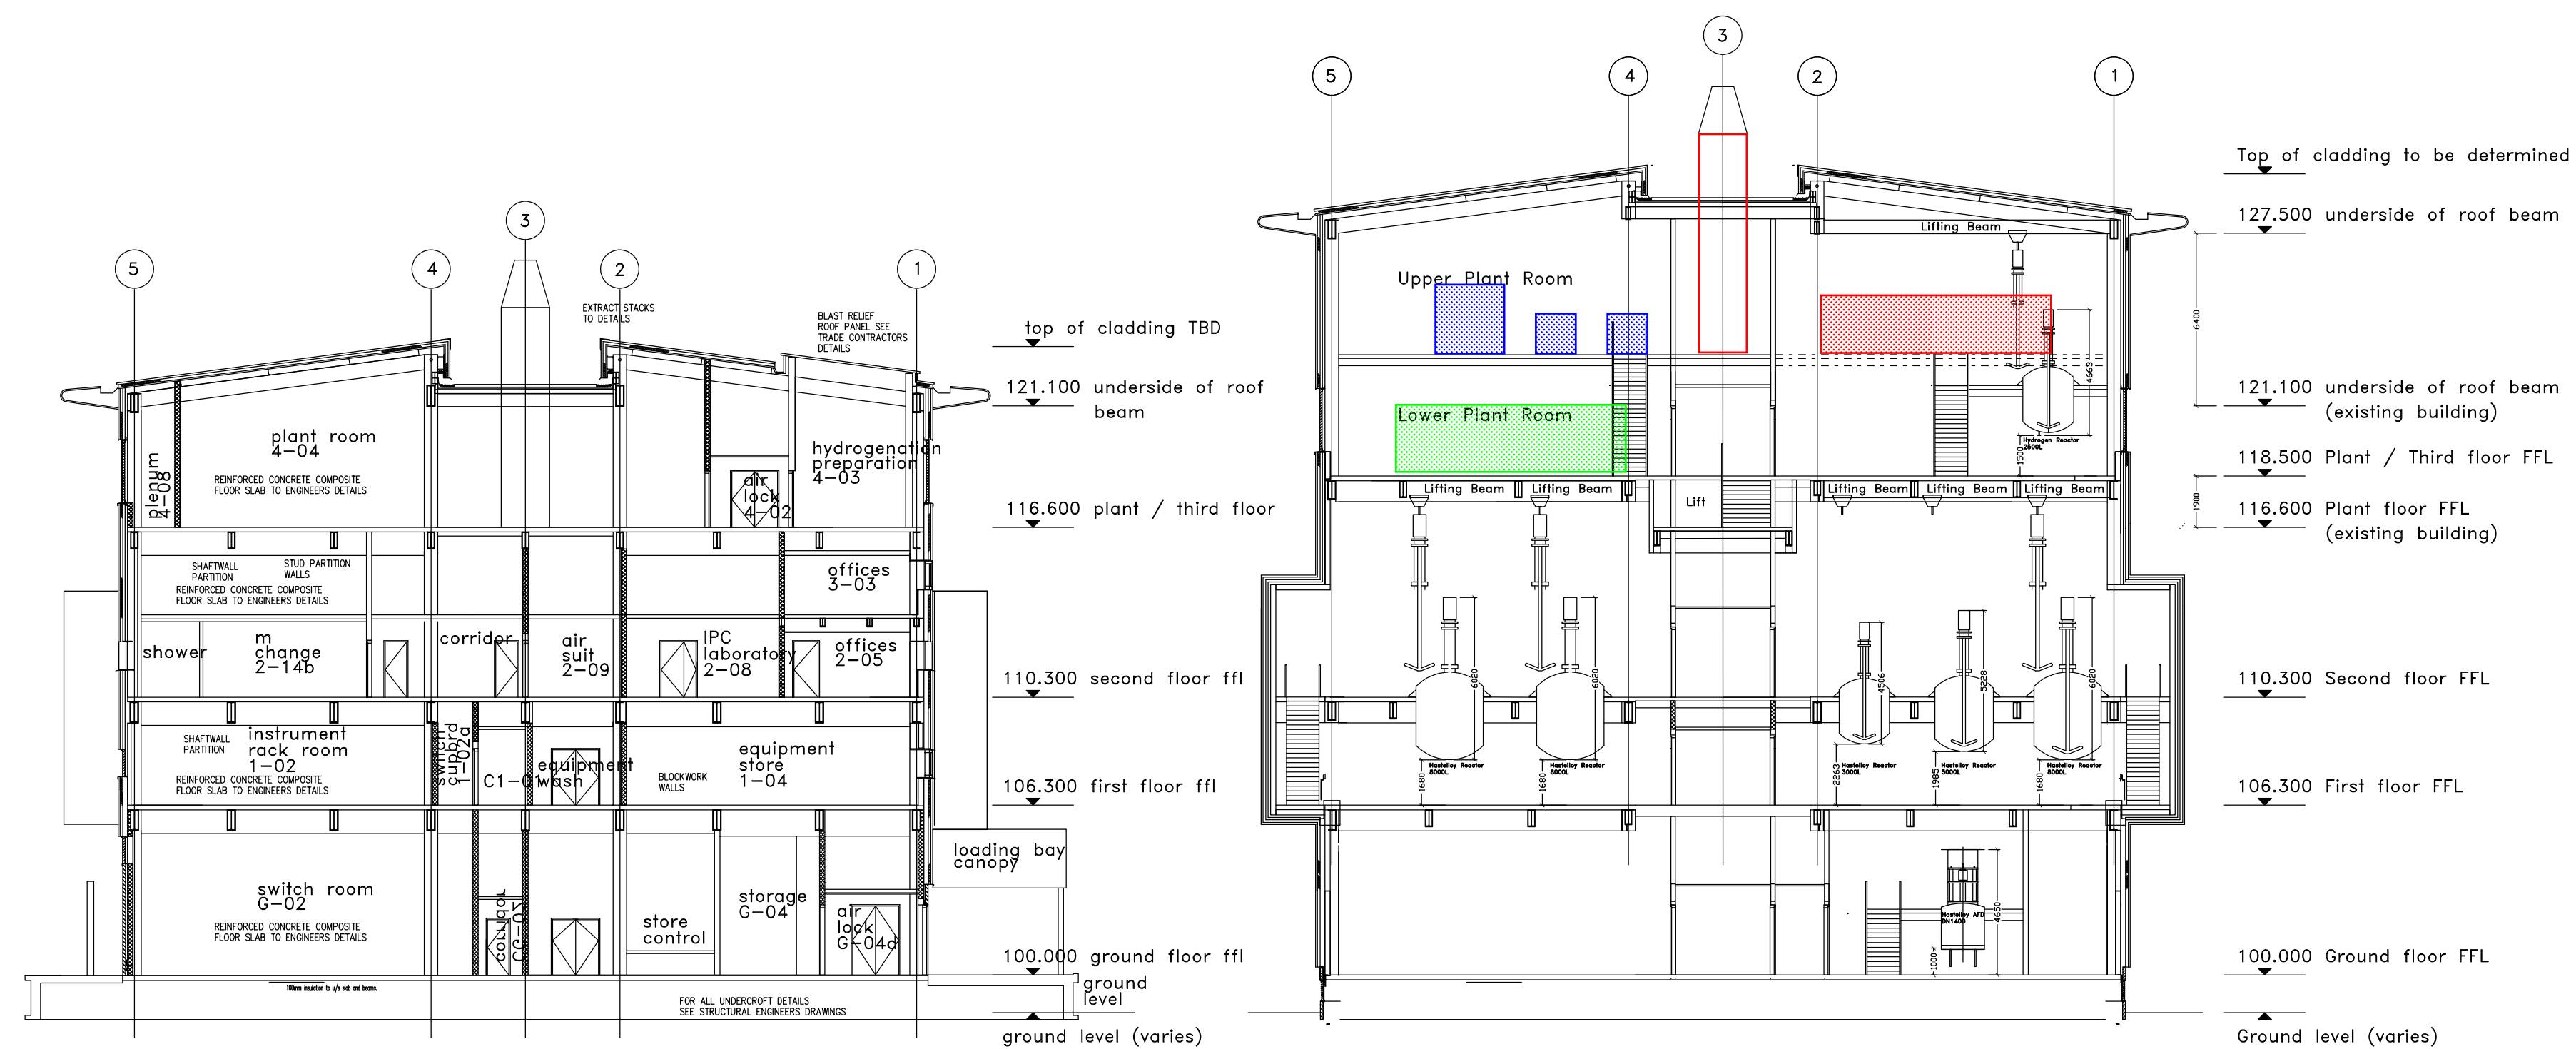

TYPICAL SECTION THROUGH OFFICE AREA
EXISTING BUILDING

TYPICAL SECTION THROUGH REACTOR SPACE
PROPOSED EXTENSION

PRESSURE REGIME & AHU ZONING SECTION