


Appendix 3 - Mechanical Drawings

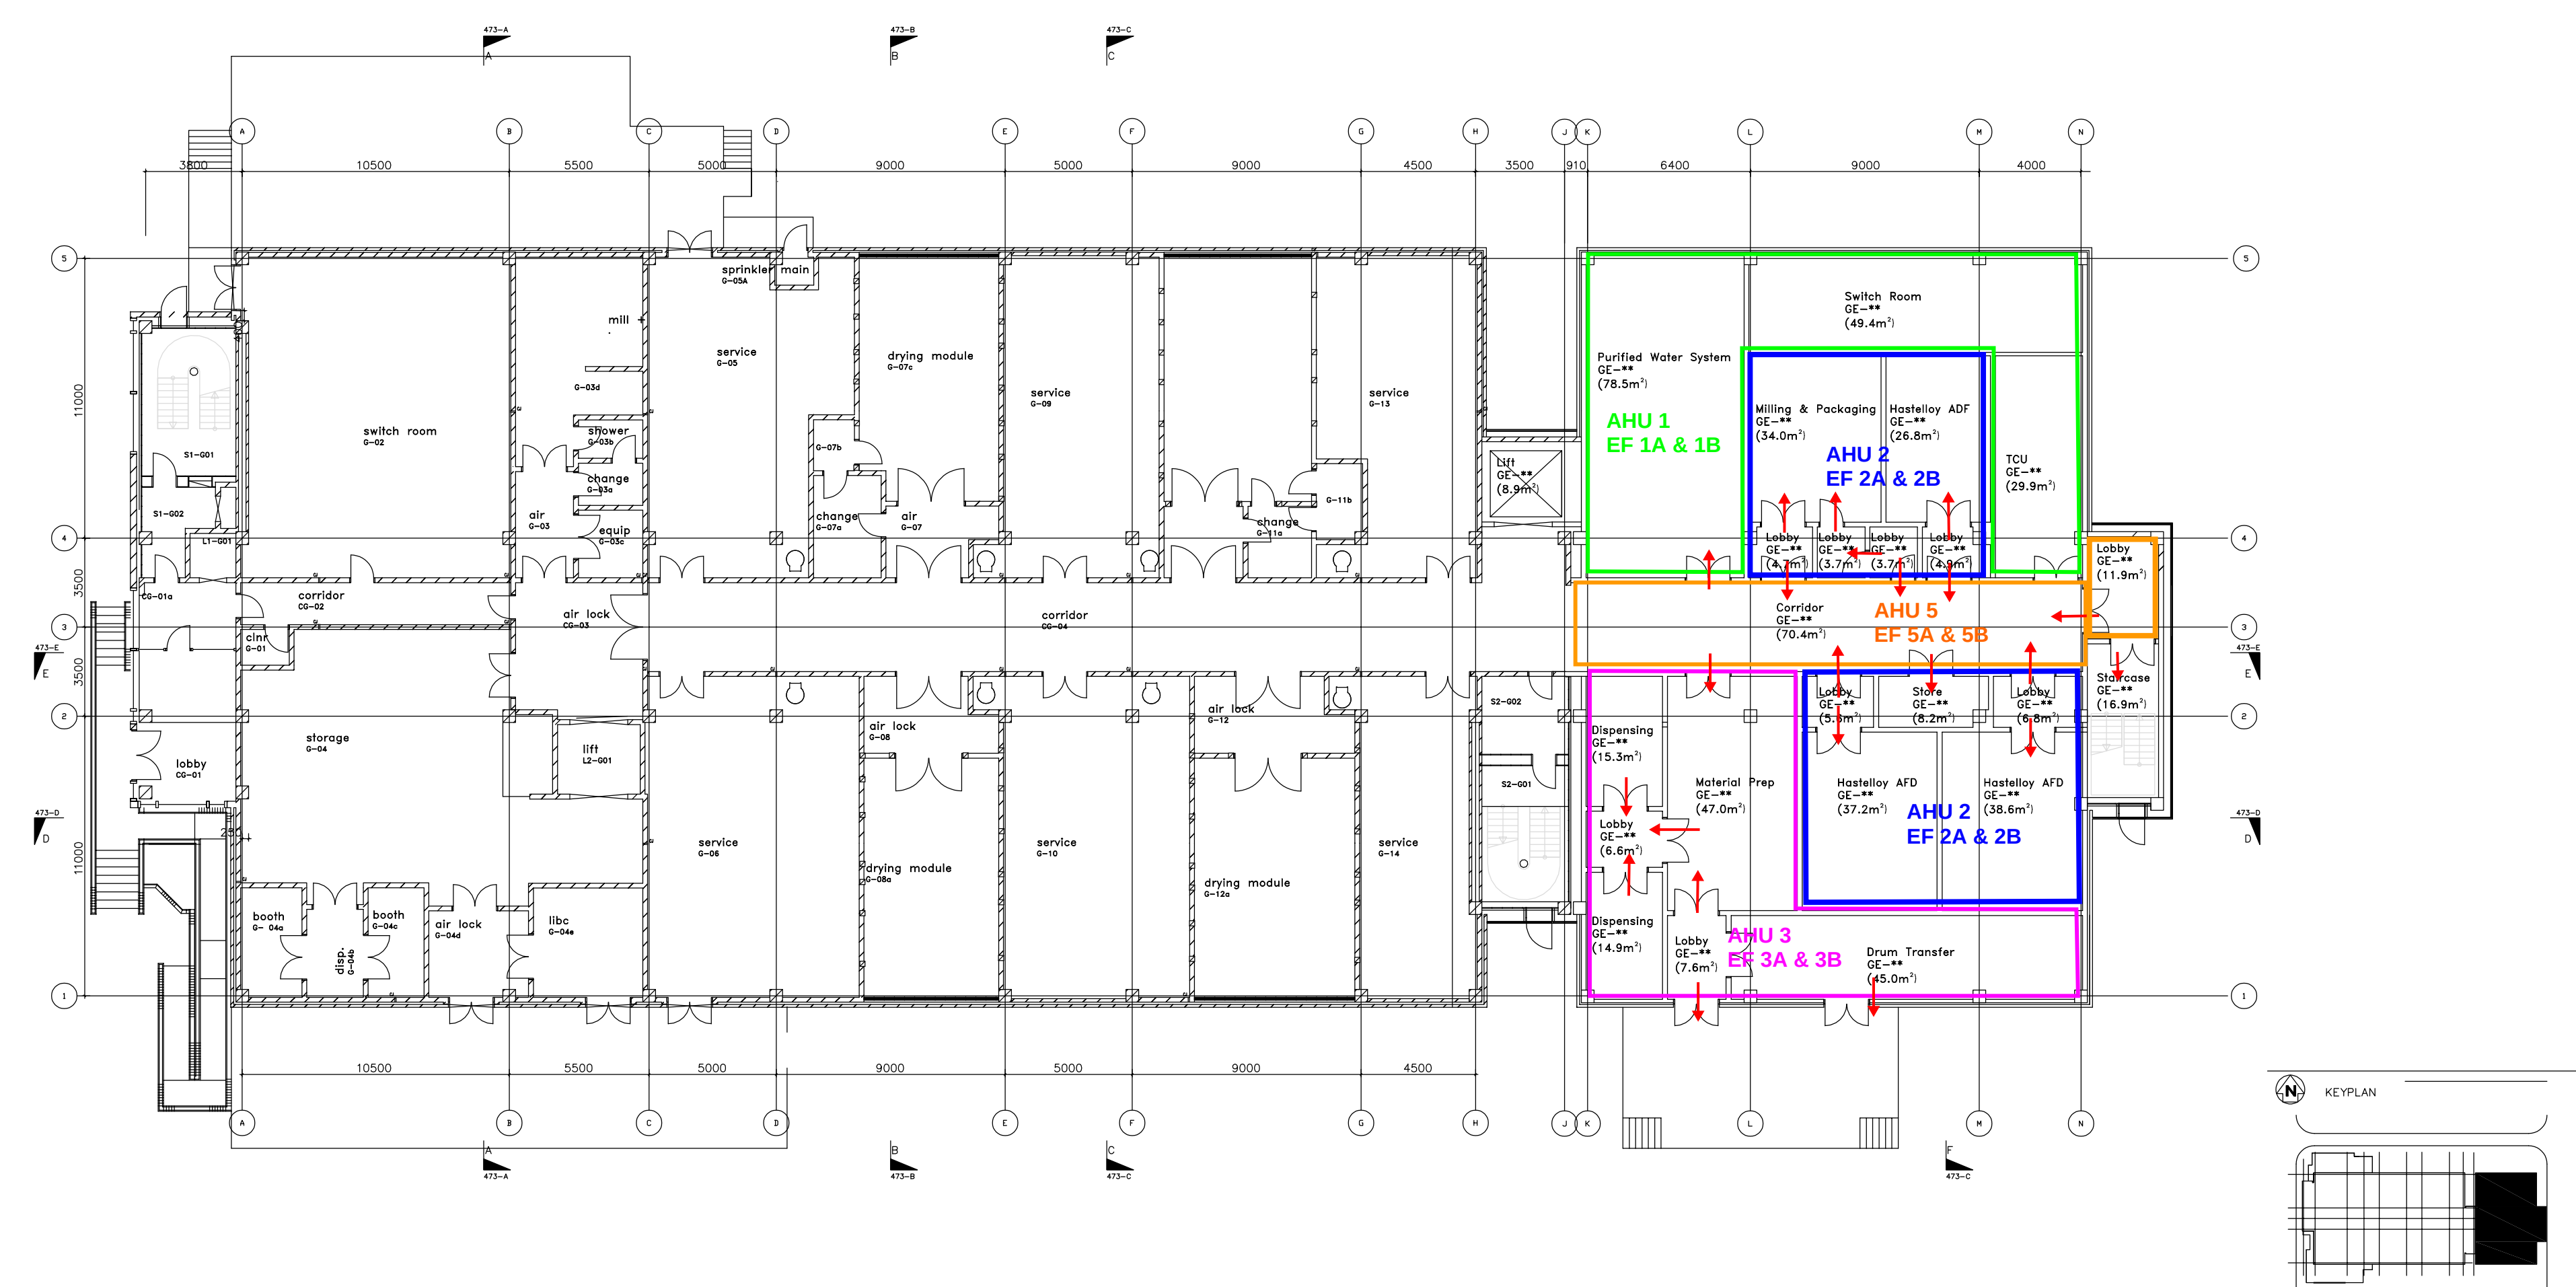

PRESSURE REGIME & AHU ZONING LAYOUT
GROUND FLOOR