


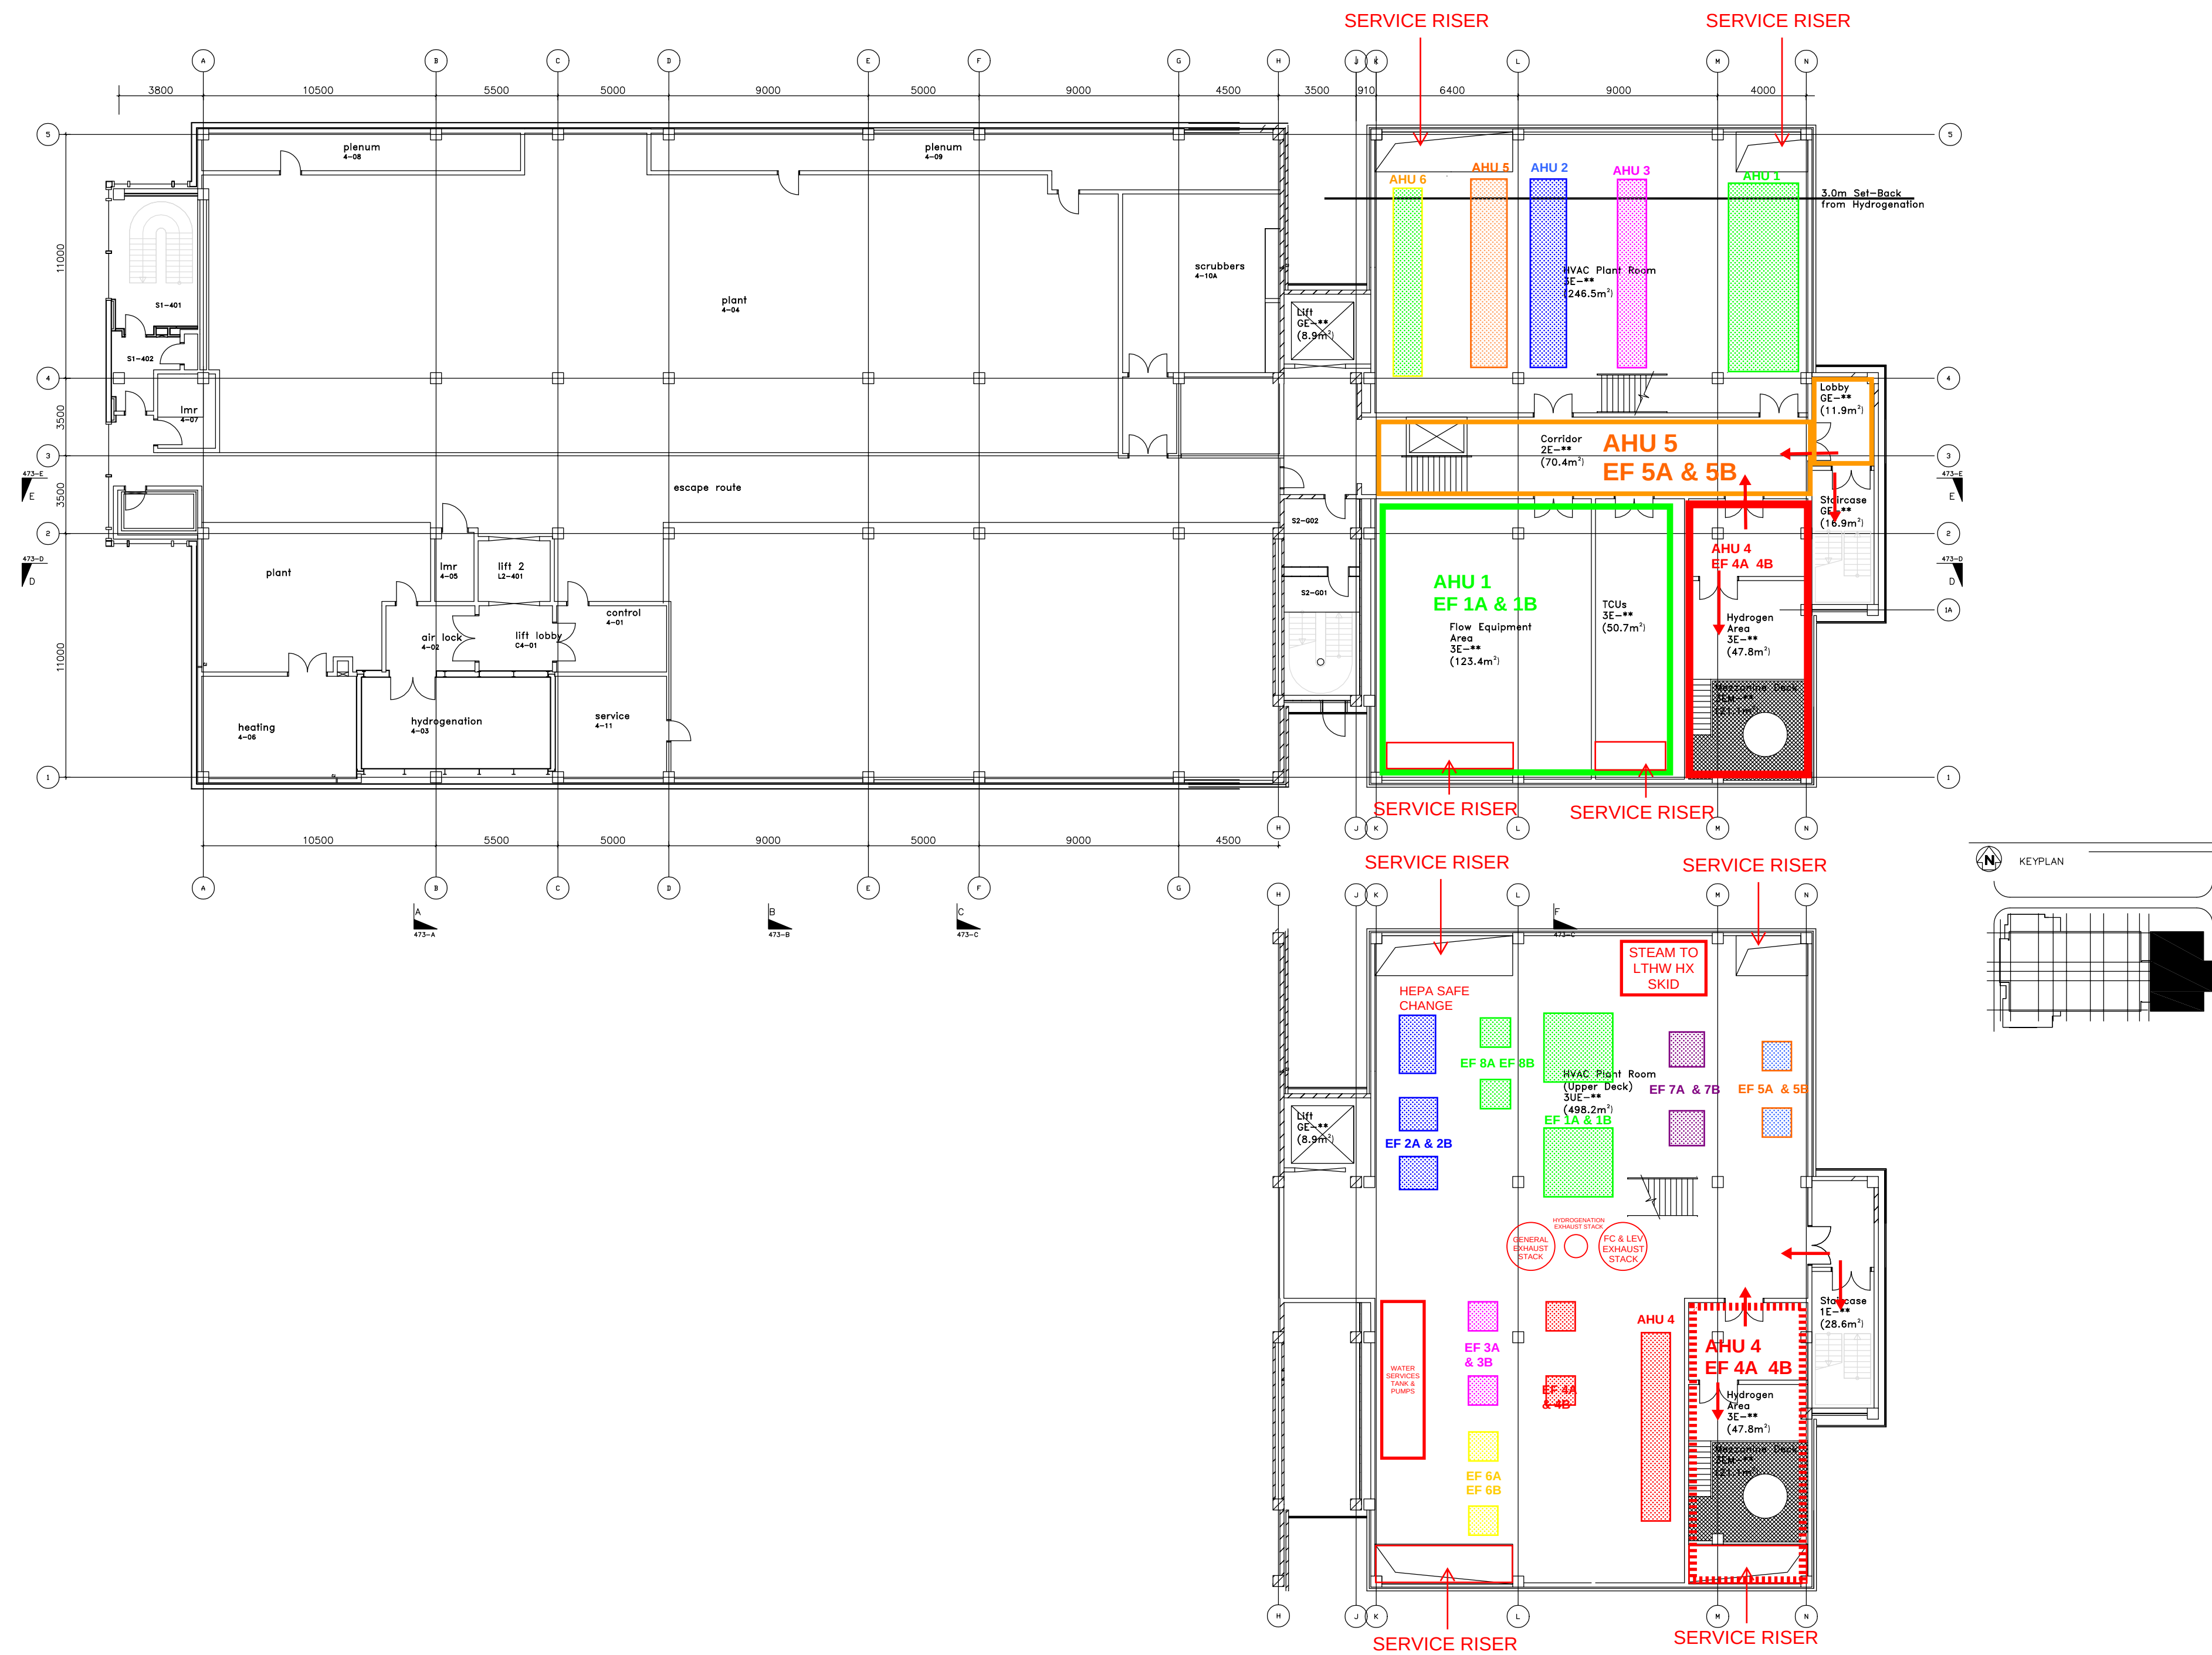

PRESSURE REGIME & AHU ZONING LAYOUT THIRD FLOOR & PLANT MEZZANINE