




Appendix 6 - Plant Setting Out Drawing

ASYMCHM NEW PLANT SETTING OUT

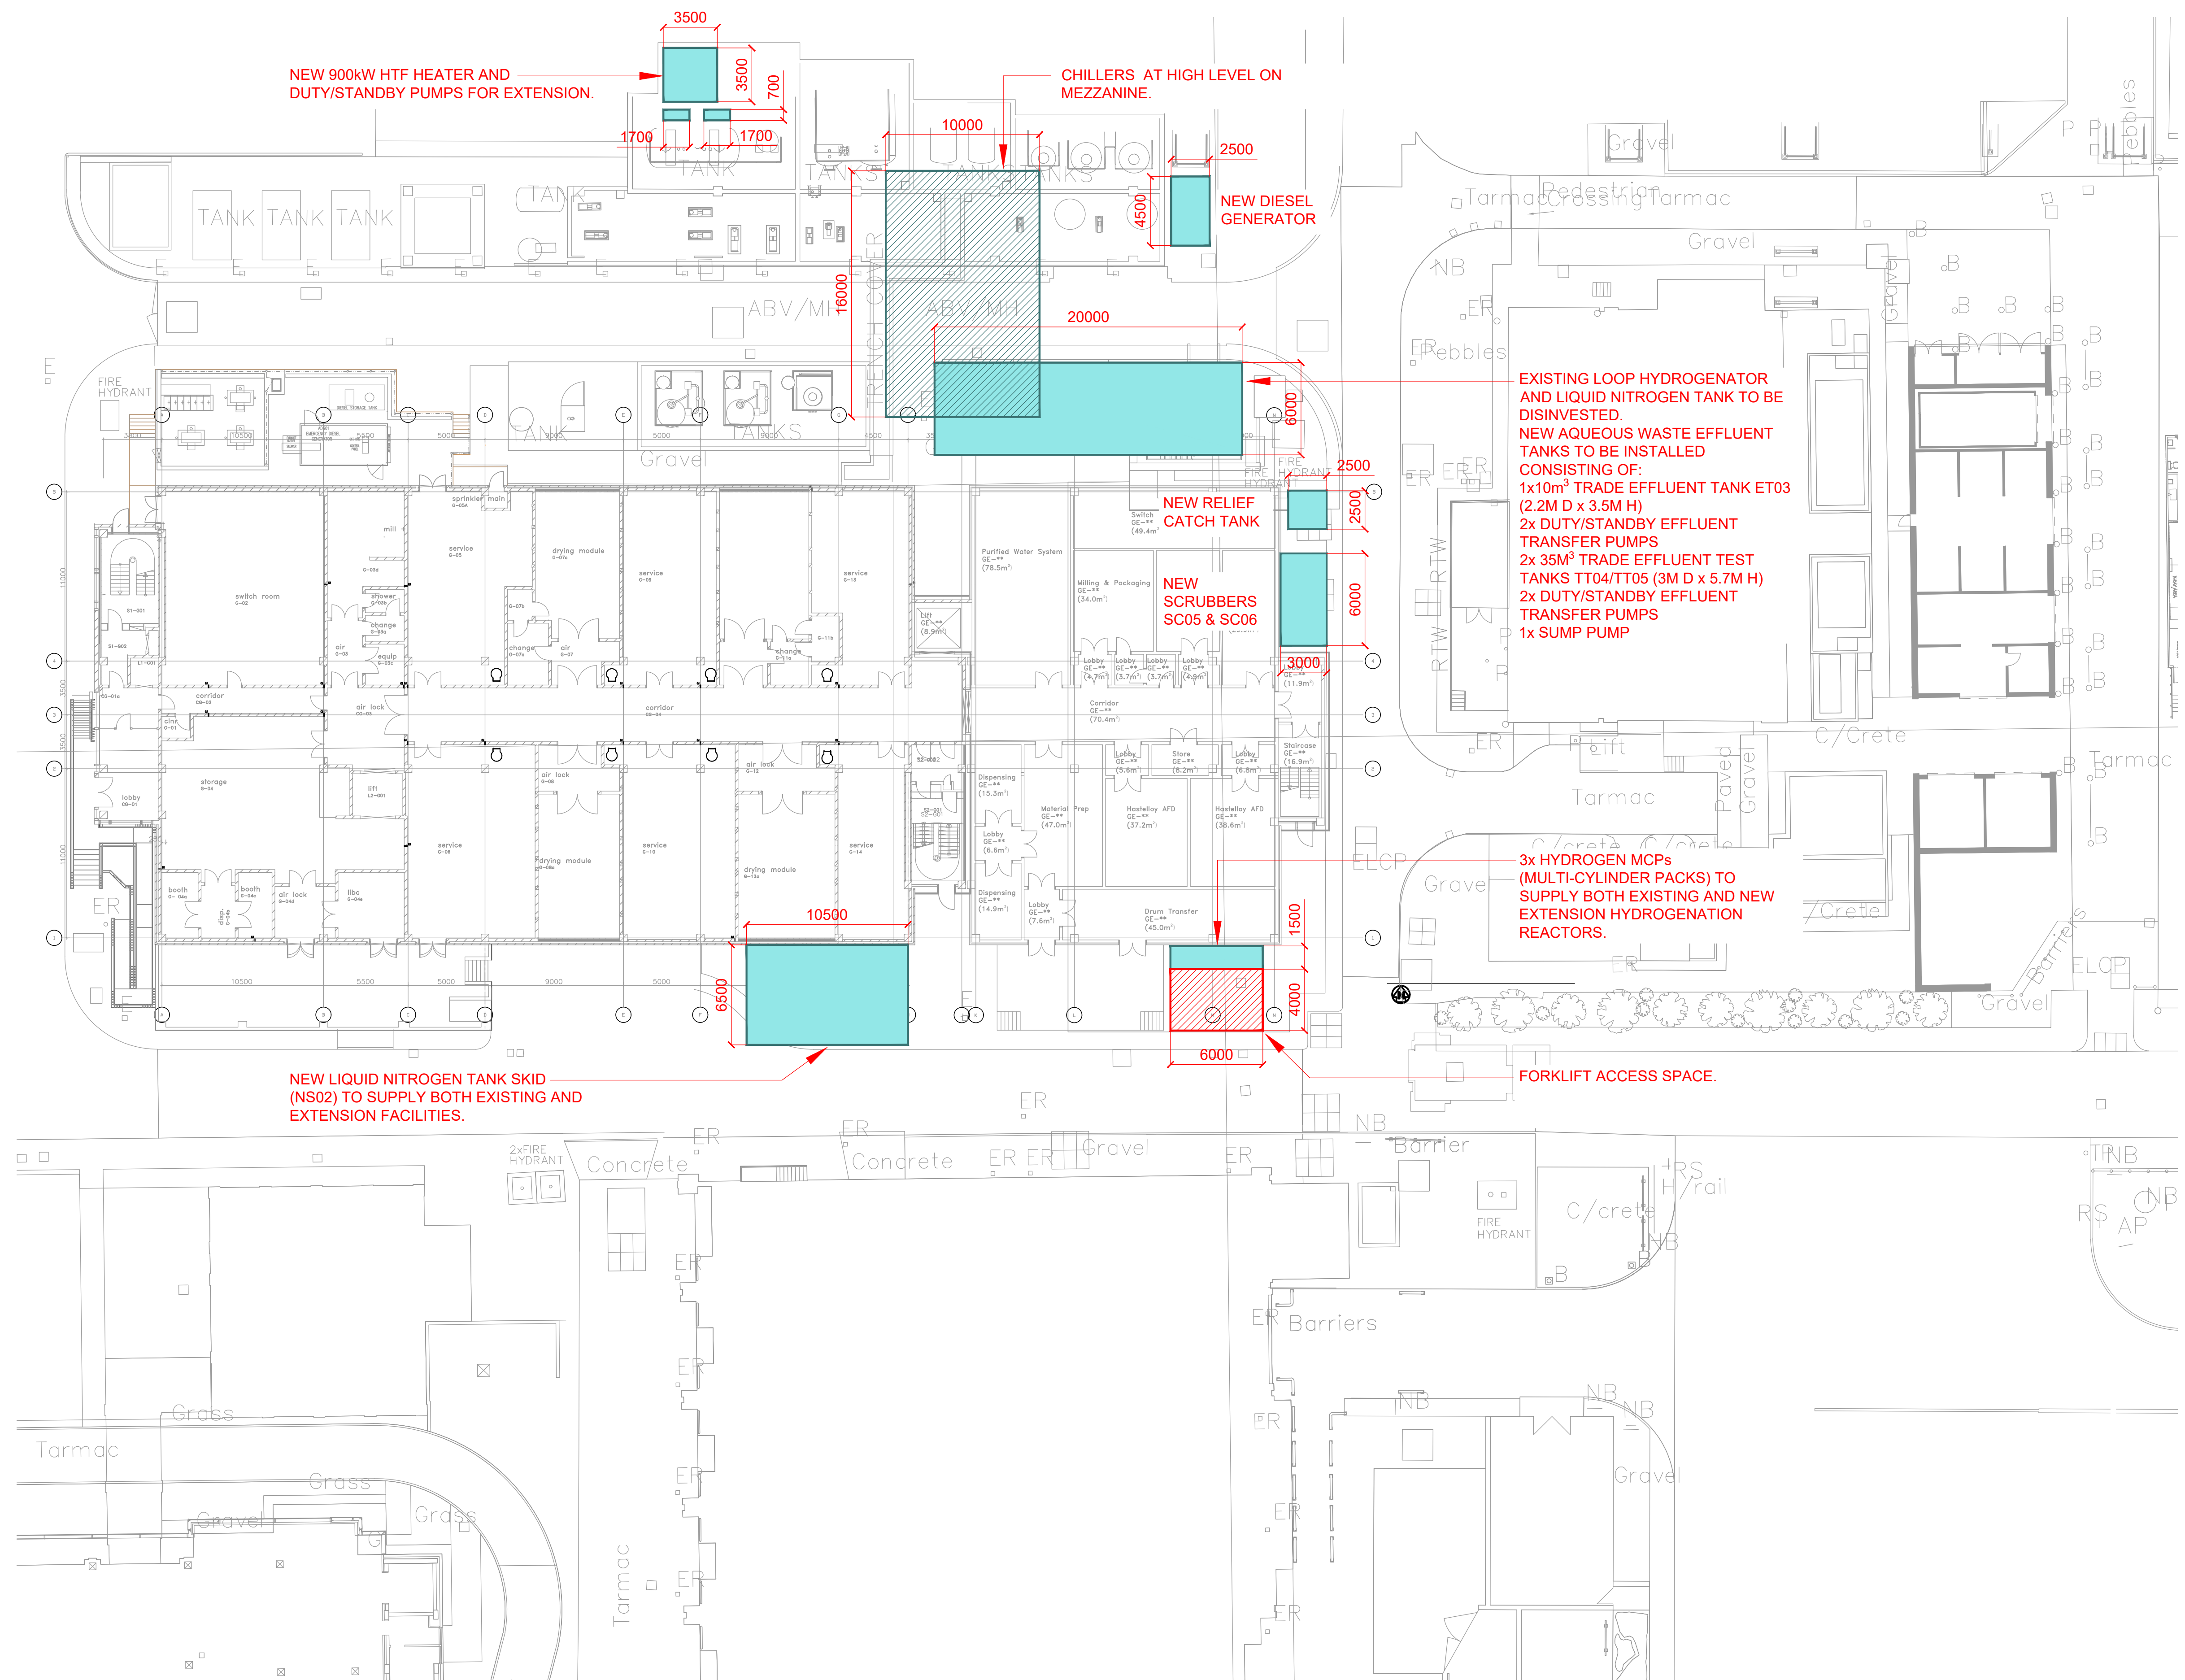

DRAWING No.: 300291-SCI-SI-XX-SK-PR-001

DATE: 07 MAY 26 SCALE: 1:200 REV: P01